


1. VENT ROUTED TO SAFE LOCATION.
 2. UPSTREAM STRAIGHT RUN MIN. 10xD. DOWNSTREAM STRAIGHT RUN MIN. 5xD.
 3. CHEMICAL CLEANING (CIP); BLEED/DRAIN CONNECTION.
 4. PRIMARY SEAL GAS IS TAKEN DOWNSTREAM LAST COMPRESSING STAGE. SKID INTERNAL DESIGN.
 5. MAX BACK-PRESSURE 0.005 BARG.
 6. OIL CHANGE BY USING TEMPORARY ARRANGEMENT WITH HOSES.
 7. INSULATION THICKNESS TO BE TAKEN INTO CONSIDERATION ON TW SELECTION.
 8. SAFETY CRITICAL HEAT TRACING - HYDRATE MITIGATION (25 DEG°C).
 9. LL SET POINT IS OVERRIDDEN AT START-UP.
 10. DELETED.
 11. DELETED.
 12. FROM SEAL GAS SYSTEM RUPTURE DISCS.
 13. DIFFERENTIAL PRESSURE BASED ORIFICE TYPE VOLUME FLOW METER.
 14. SECONDARY SEAL GAS AND SEPARATION GAS. 6"-VA-63-9037-AS205-00
 15. HIGH POINT VENT AND LOW POINT DRAIN TO BE FINALIZED BY PIPING AS PER PIPING LAYOUT.
 16. MANUAL DRAIN PRIOR TO EACH START-UP. PUSH BUTTON WITH PERMISSIVE FOR START-UP SEQUENCE.
 17. PROVISION FOR FUTURE HOT GAS BYPASS LINE.
 18. LUBE OIL RESERVOIR VENT, OIL MIST SEPARATOR INSTALLED OFF-SKID.
 19. FLAME ARRESTER INCLUDES FLAME FILTER AND LOCATED AT END OF PIPE.
 20. ATMOSPHERIC VENT.
 21. THIS P&ID CONTAINS DCN-KP-0273-1.
- FIT 9020 26

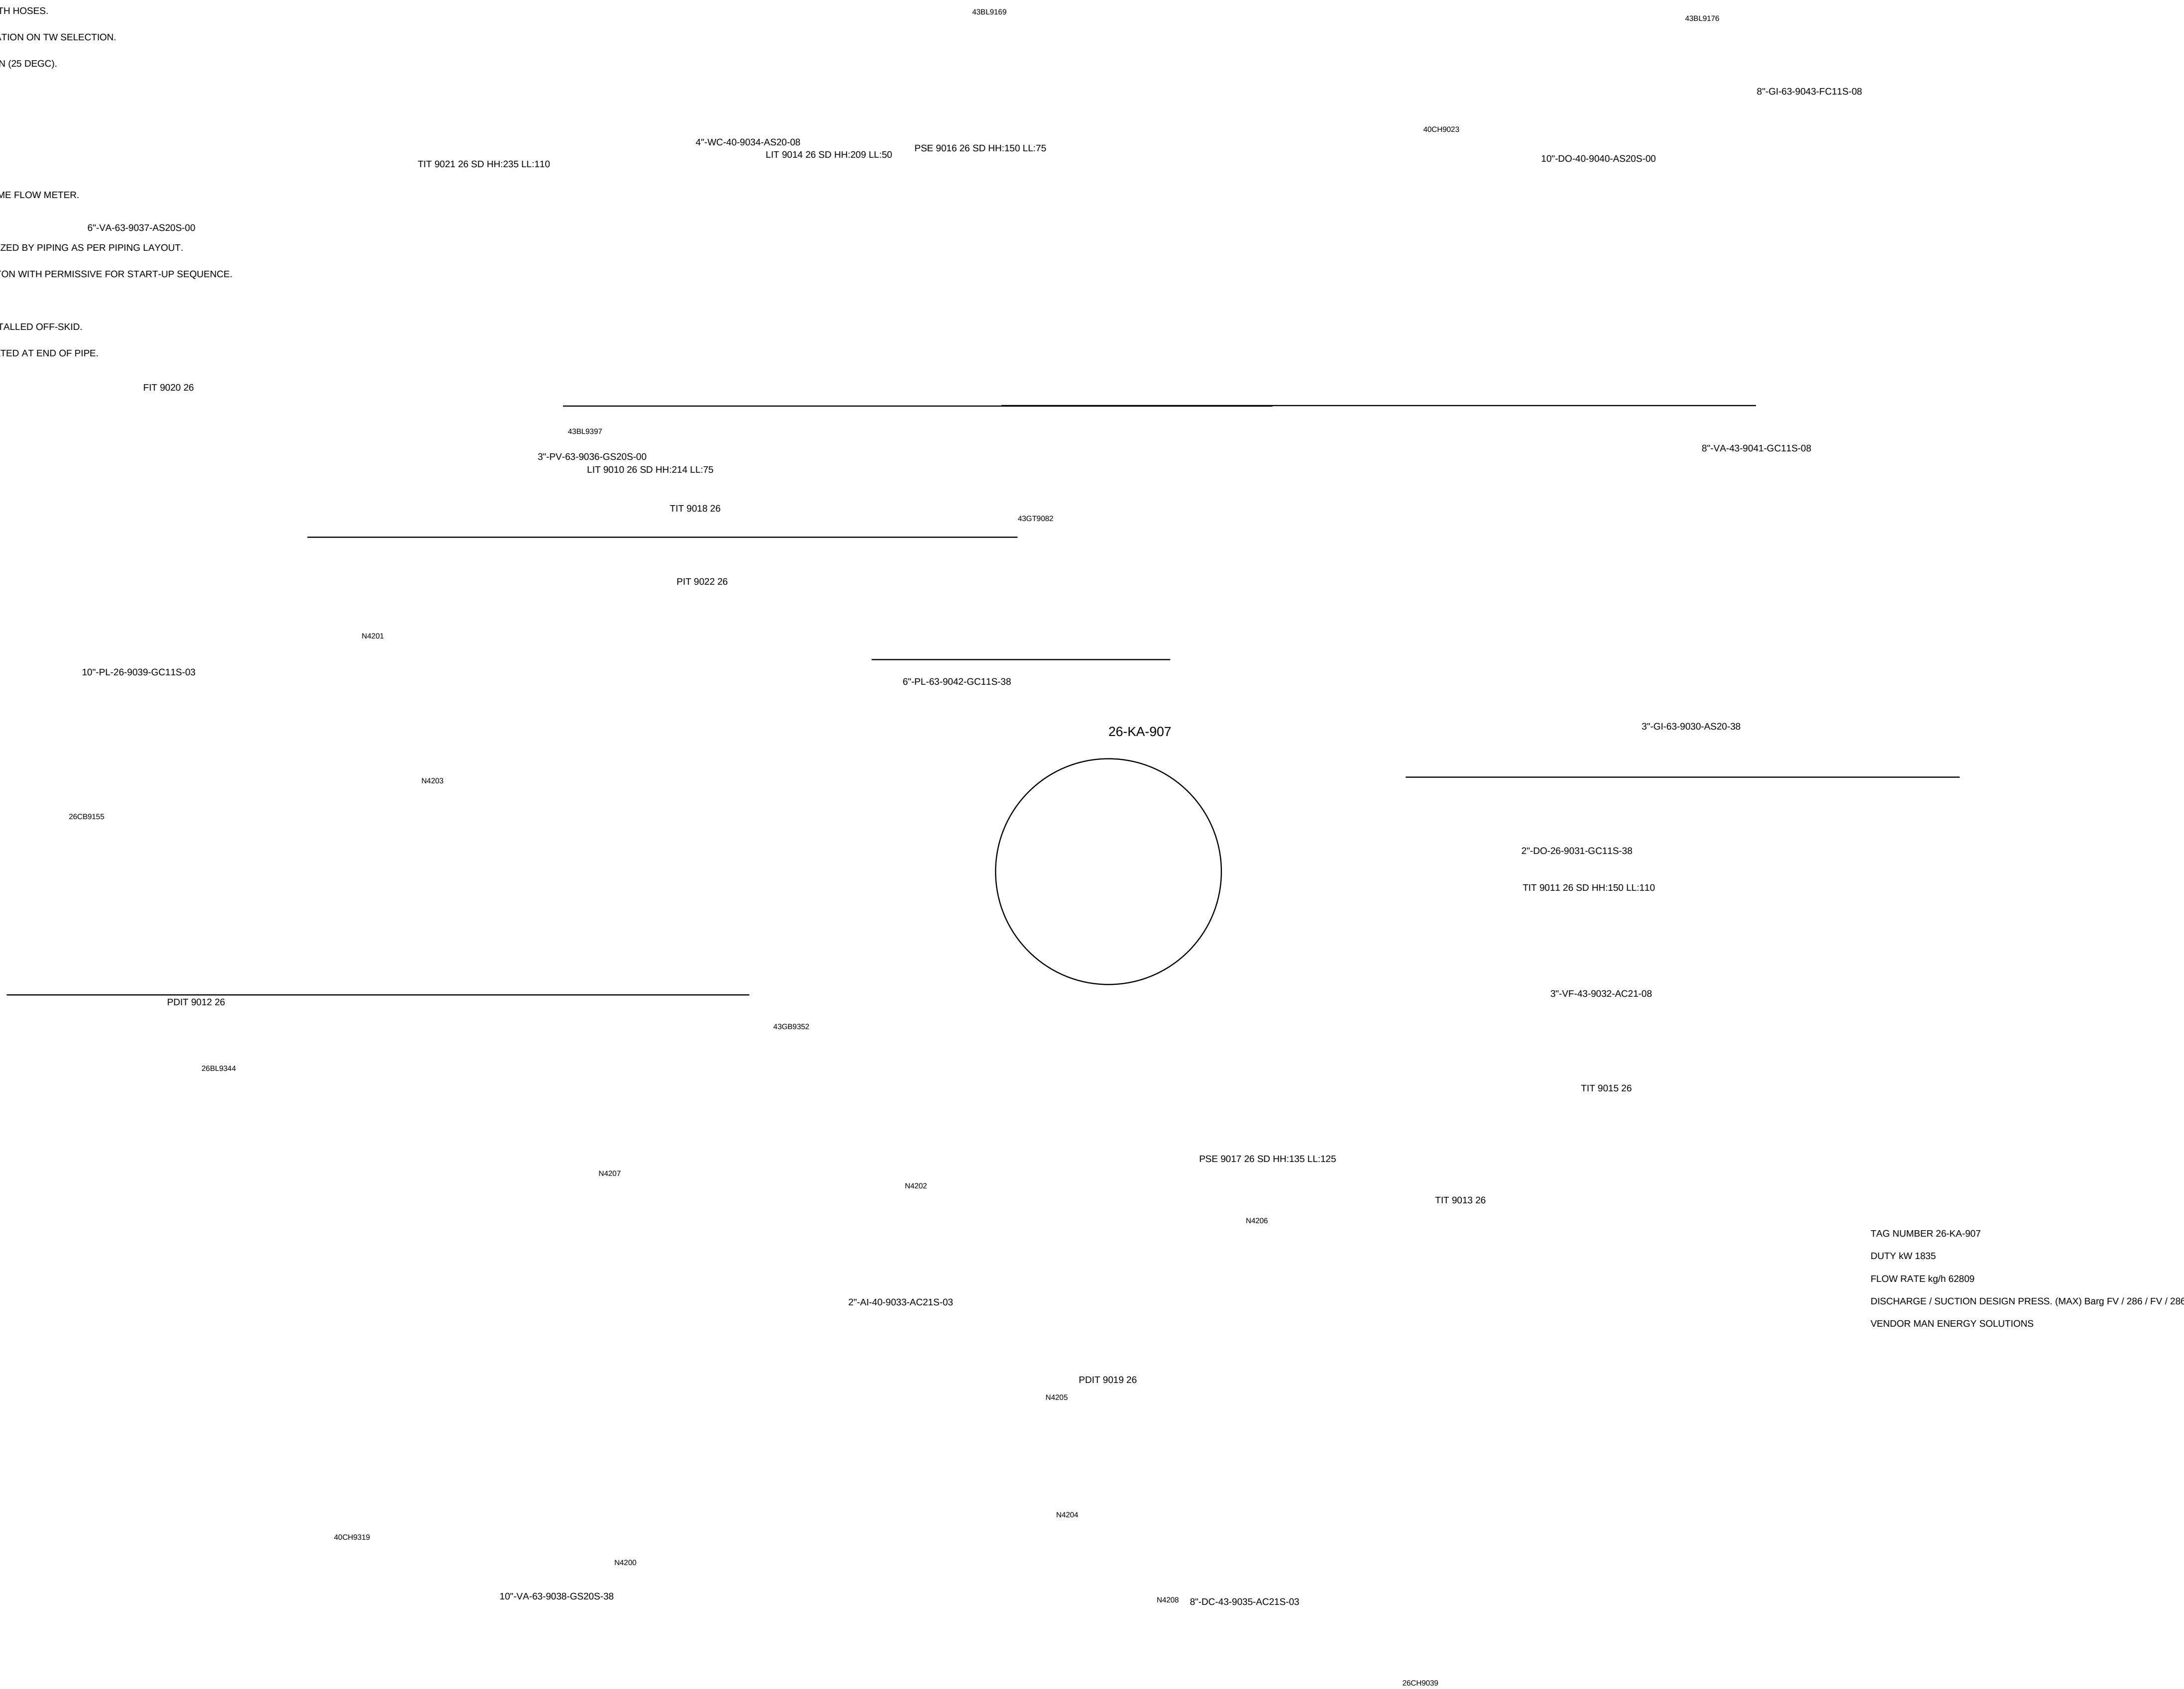

A 2026-01-15 ISSUED FOR DESIGN

2026-01-15

SHEET 1 OF 1

REV A

26-KA-907

3RD STAGE HP GAS EXPORT COMPRESSOR

0D204-PID-26-907-001