


1. VENT ROUTED TO SAFE LOCATION.
2. UPSTREAM STRAIGHT RUN MIN. 10xID. DOWNSTREAM STRAIGHT RUN MIN. 5xID.
3. CHEMICAL CLEANING (CIP); BLEED/DRAIN CONNECTION.
4. PRIMARY SEAL GAS IS TAKEN DOWNSTREAM LAST COMPRESSING STAGE. SKID INTERNAL DESIGN.
5. MAX BACK-PRESSURE 0.005 BARG.
6. OIL CHANGE BY USING TEMPORARY ARRANGEMENT WITH HOSES.
7. INSULATION THICKNESS TO BE TAKEN INTO CONSIDERATION ON TW SELECTION.
8. SAFETY CRITICAL HEAT TRACING - HYDRATE MITIGATION (25 DEG.C).
9. LL SET POINT IS OVERRIDDEN AT START-UP.
10. DELETED.
11. DELETED.
12. FROM SEAL GAS SYSTEM RUPTURE DISCS.
13. DIFFERENTIAL PRESSURE BASED ORIFICE TYPE VOLUME FLOW METER.
14. SECONDARY SEAL GAS AND SEPARATION GAS. 6" VA-63-9037-AS205-00
15. HIGH POINT VENT AND LOW POINT DRAIN TO BE FINALIZED BY PIPING AS PER PIPING LAYOUT.
16. MANUAL DRAIN PRIOR TO EACH START-UP. PUSH BUTTON WITH PERMISSIVE FOR START-UP SEQUENCE.
17. PROVISION FOR FUTURE HOT GAS BYPASS LINE.
18. LUBE OIL RESERVOIR VENT. OIL MIST SEPARATOR INSTALLED OFF-SKID.
19. FLAME ARRESTER INCLUDES FLAME FILTER AND LOCATED AT END OF PIPE.
20. ATMOSPHERIC VENT.
21. THIS P&ID CONTAINS DGN-KP-0273-1.

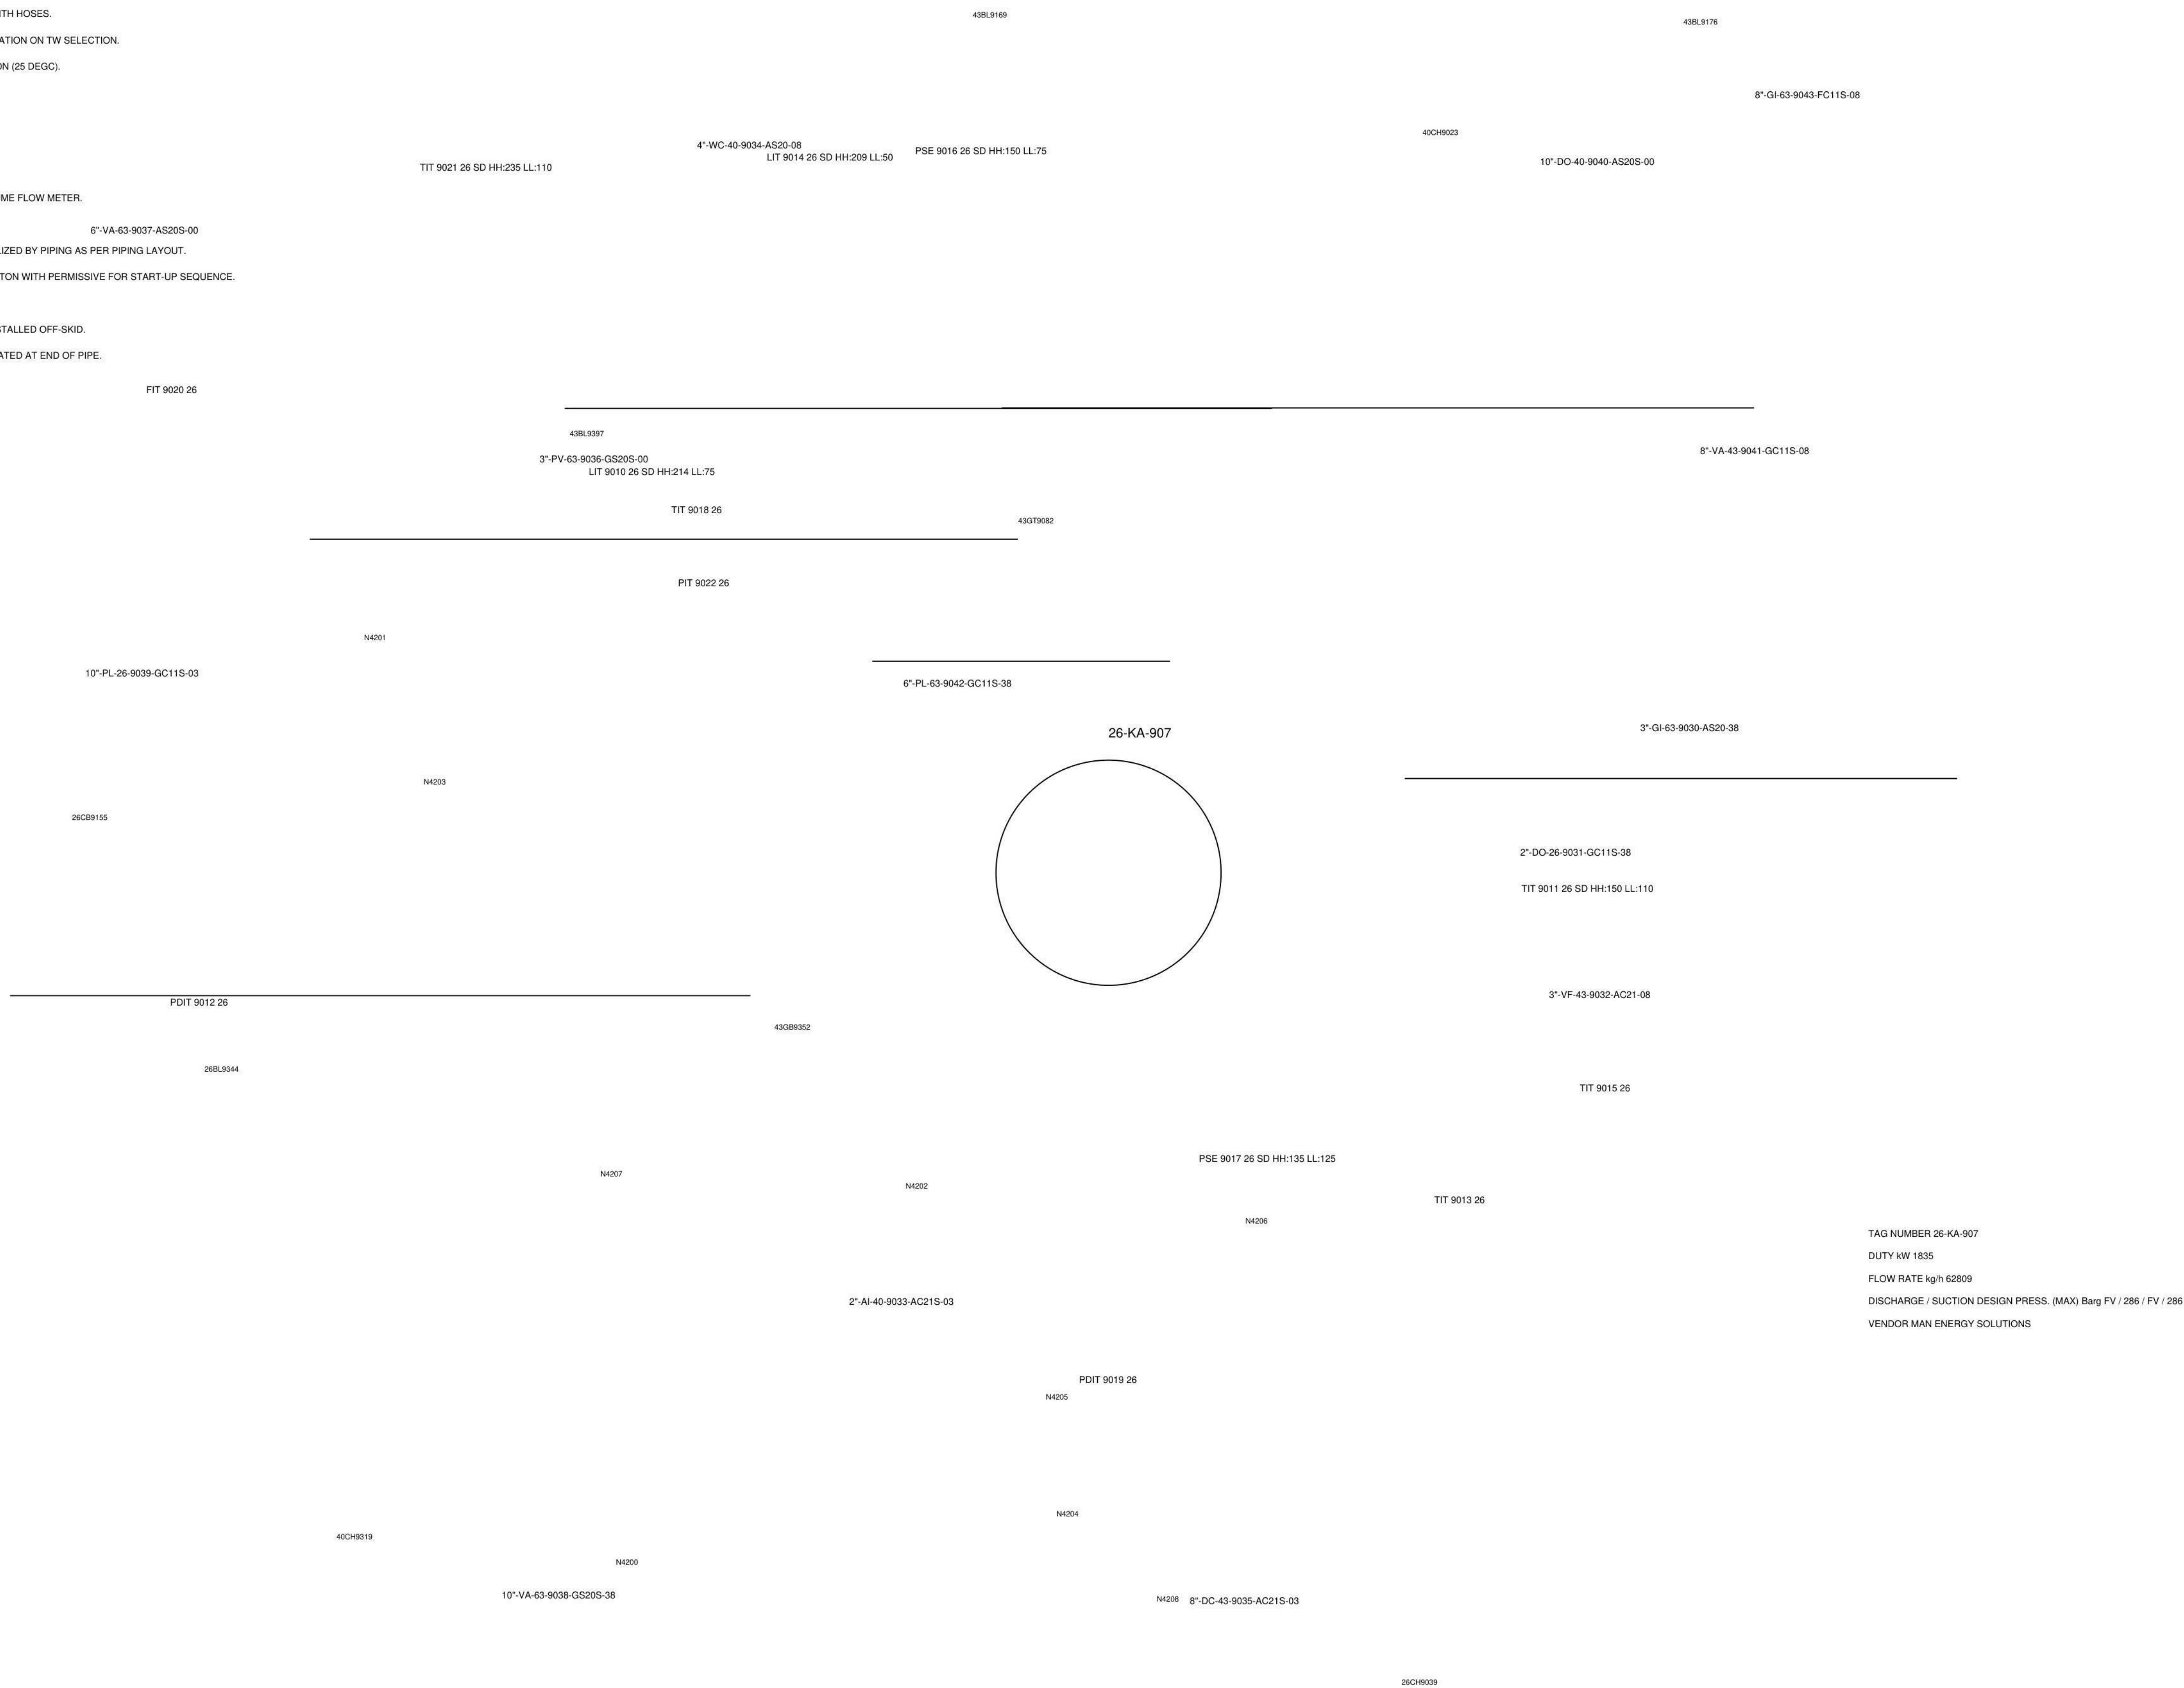

A 2026-01-15 ISSUED FOR DESIGN

2026-01-15

SHEET 1 OF 1

REV A

26-KA-907

3RD STAGE HP GAS EXPORT COMPRESSOR

0D204-PID-26-907-001