


1. OIL CHANGE BY USING TEMPORARY ARRANGEMENT WITH HOSES.
2. FROM SEAL GAS SYSTEM RUPTURE DISCS.
3. MAX BACK-PRESSURE 1.5 BARG.
4. HIGH POINT VENT AND LOW POINT DRAIN TO BE FINALIZED BY PIPING AS PER PIPING LAYOUT.
5. DELETED.
6. DELETED.
7. MAX BACK-PRESSURE 0.005 BARG.
8. UPSTREAM STRAIGHT RUN MIN. 10xD, DOWNSTREAM STRAIGHT RUN MIN. 5xD.
9. LL SET POINT IS OVERRIDEN AT START-UP.
10. INSULATION THICKNESS TO BE TAKEN INTO CONSIDERATION ON TW SELECTION.
11. DELETED.
12. LUBE OIL RESERVOIR VENT. OIL MIST SEPARATOR INSTALLED OFF-SKID.
13. ATMOSPHERIC VENT.
14. VENT ROUTED TO SAFE LOCATION.
15. BOTTOM ENTRY FOR SUCTION AND DISCHARGE NOZZLES.
16. THIS P&ID CONTAINS DCN-KP-0273-1.

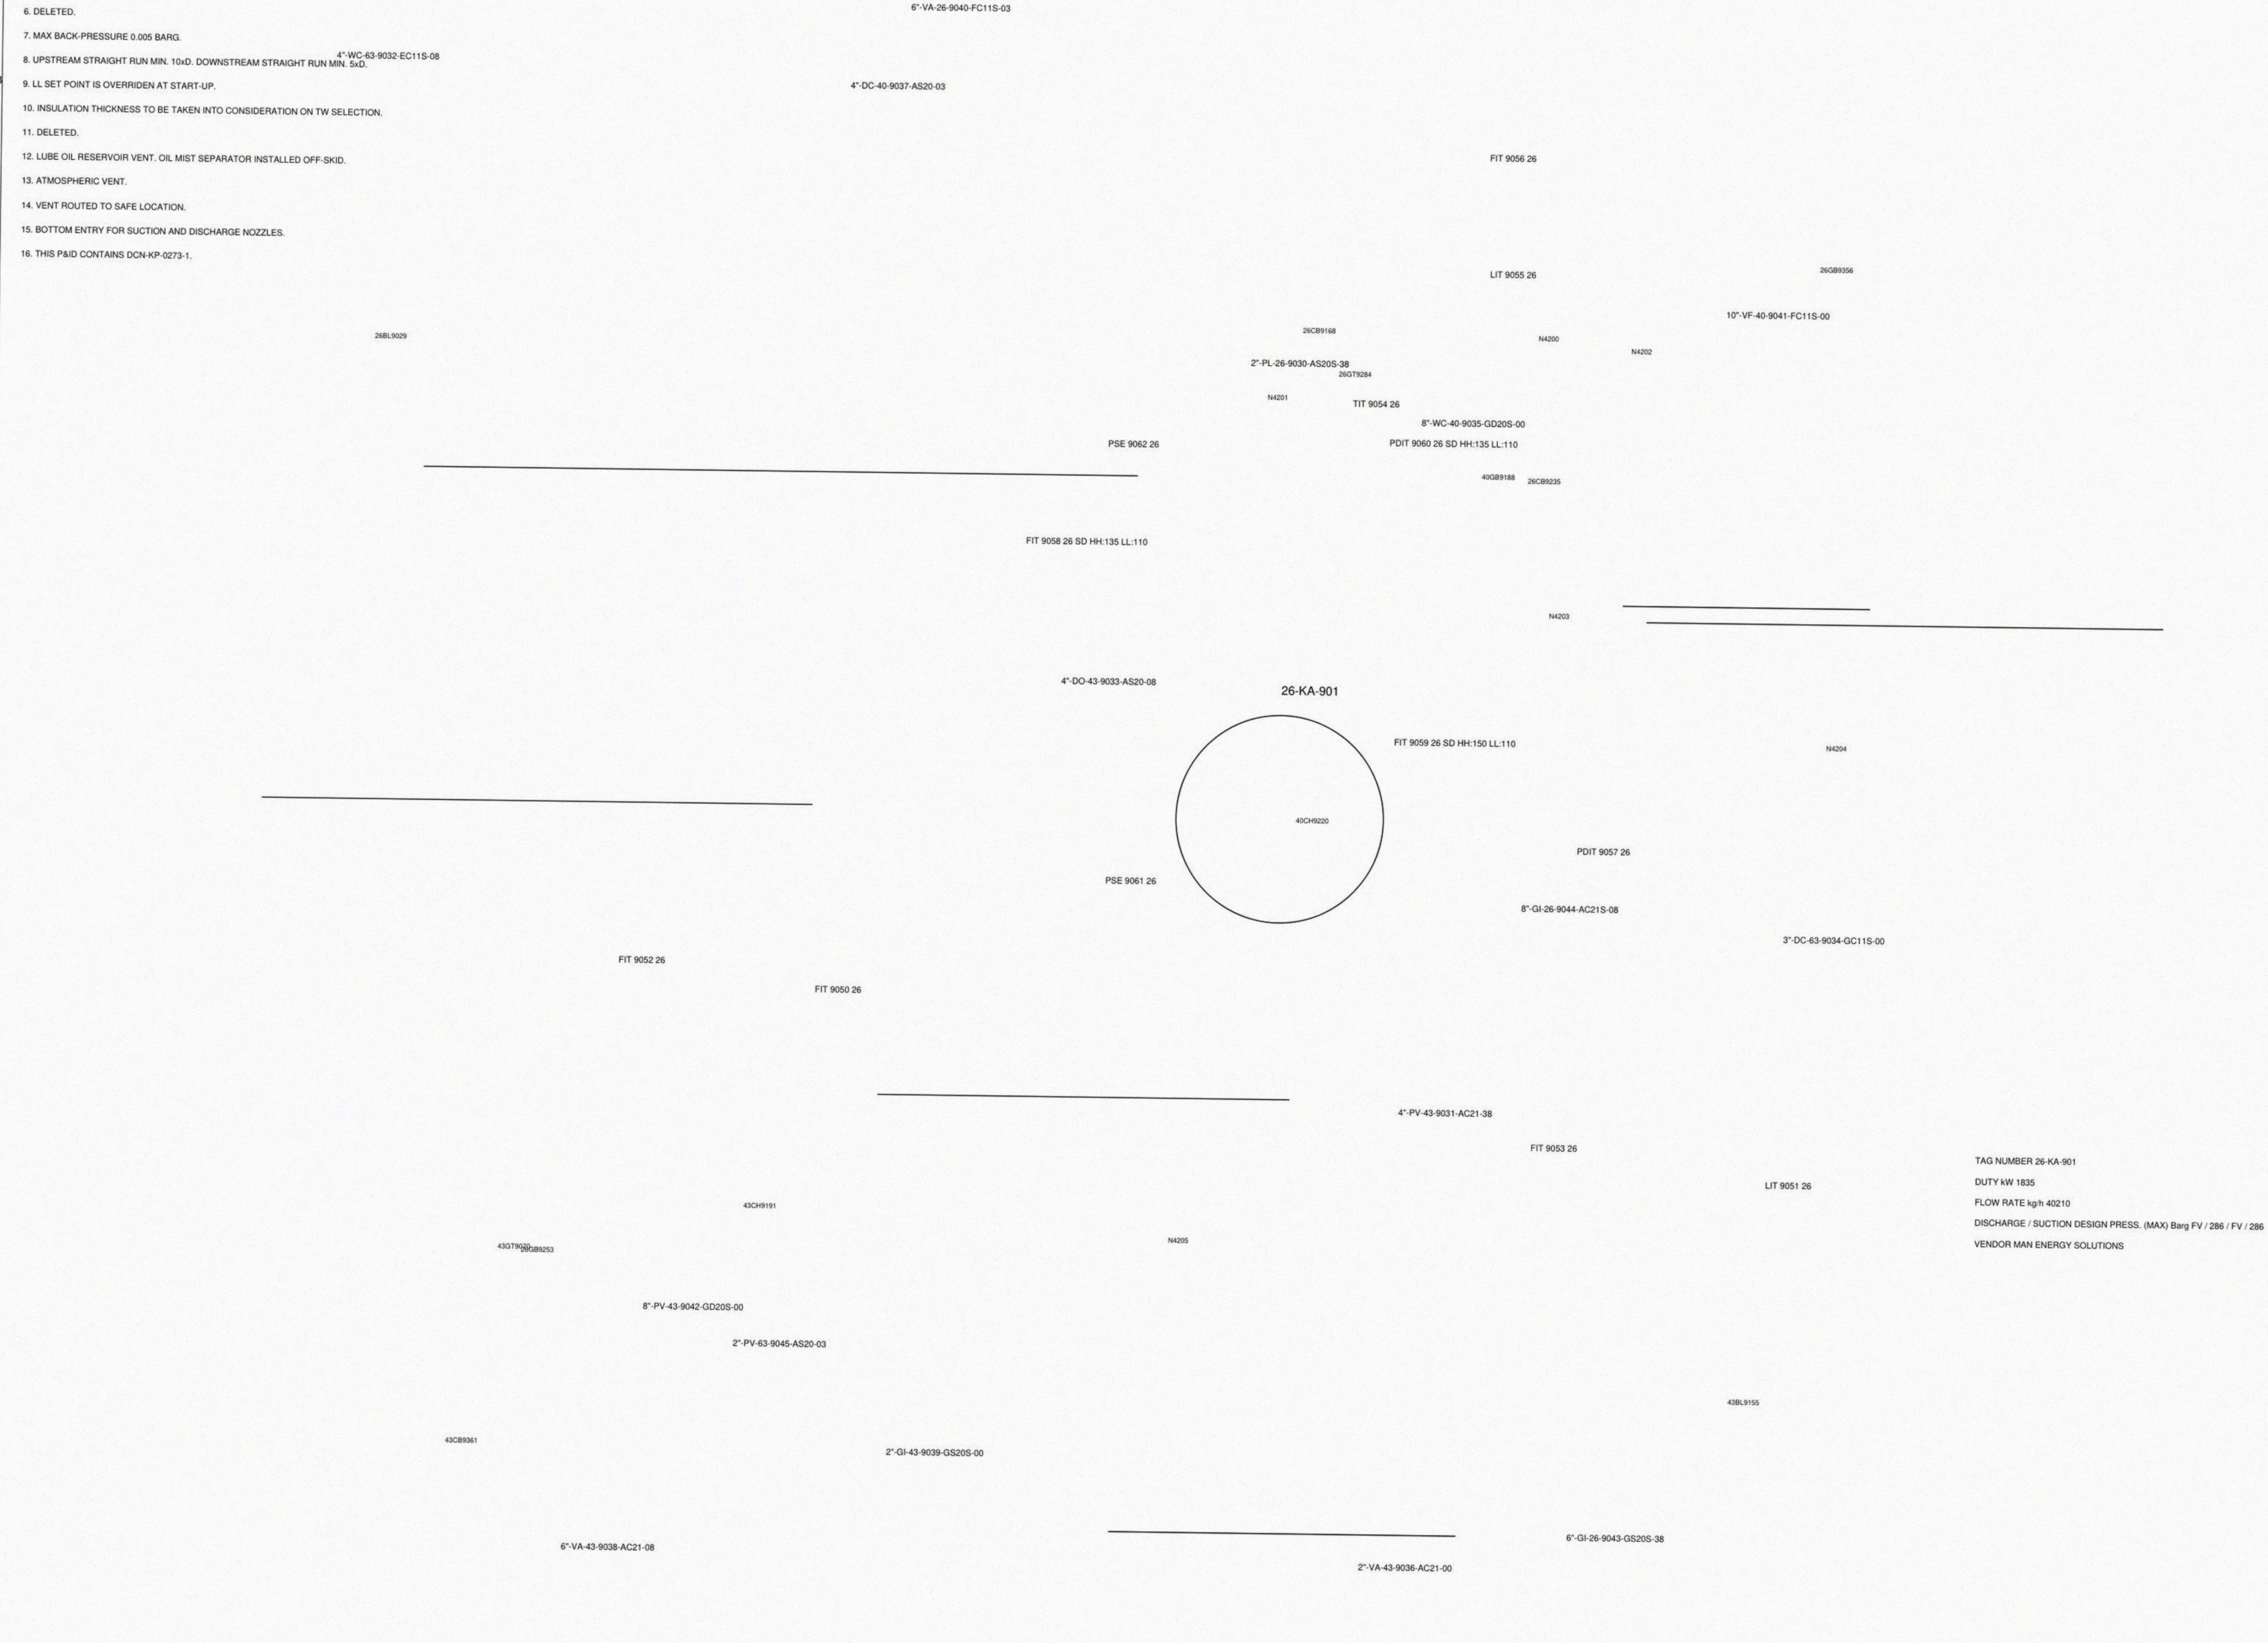

TAG NUMBER 26-KA-901
DUTY kW 1835
FLOW RATE kg/h 40210
DISCHARGE / SUCTION DESIGN PRESS. (MAX) Barg FV / 286 / FV / 286
VENDOR MAN ENERGY SOLUTIONS