


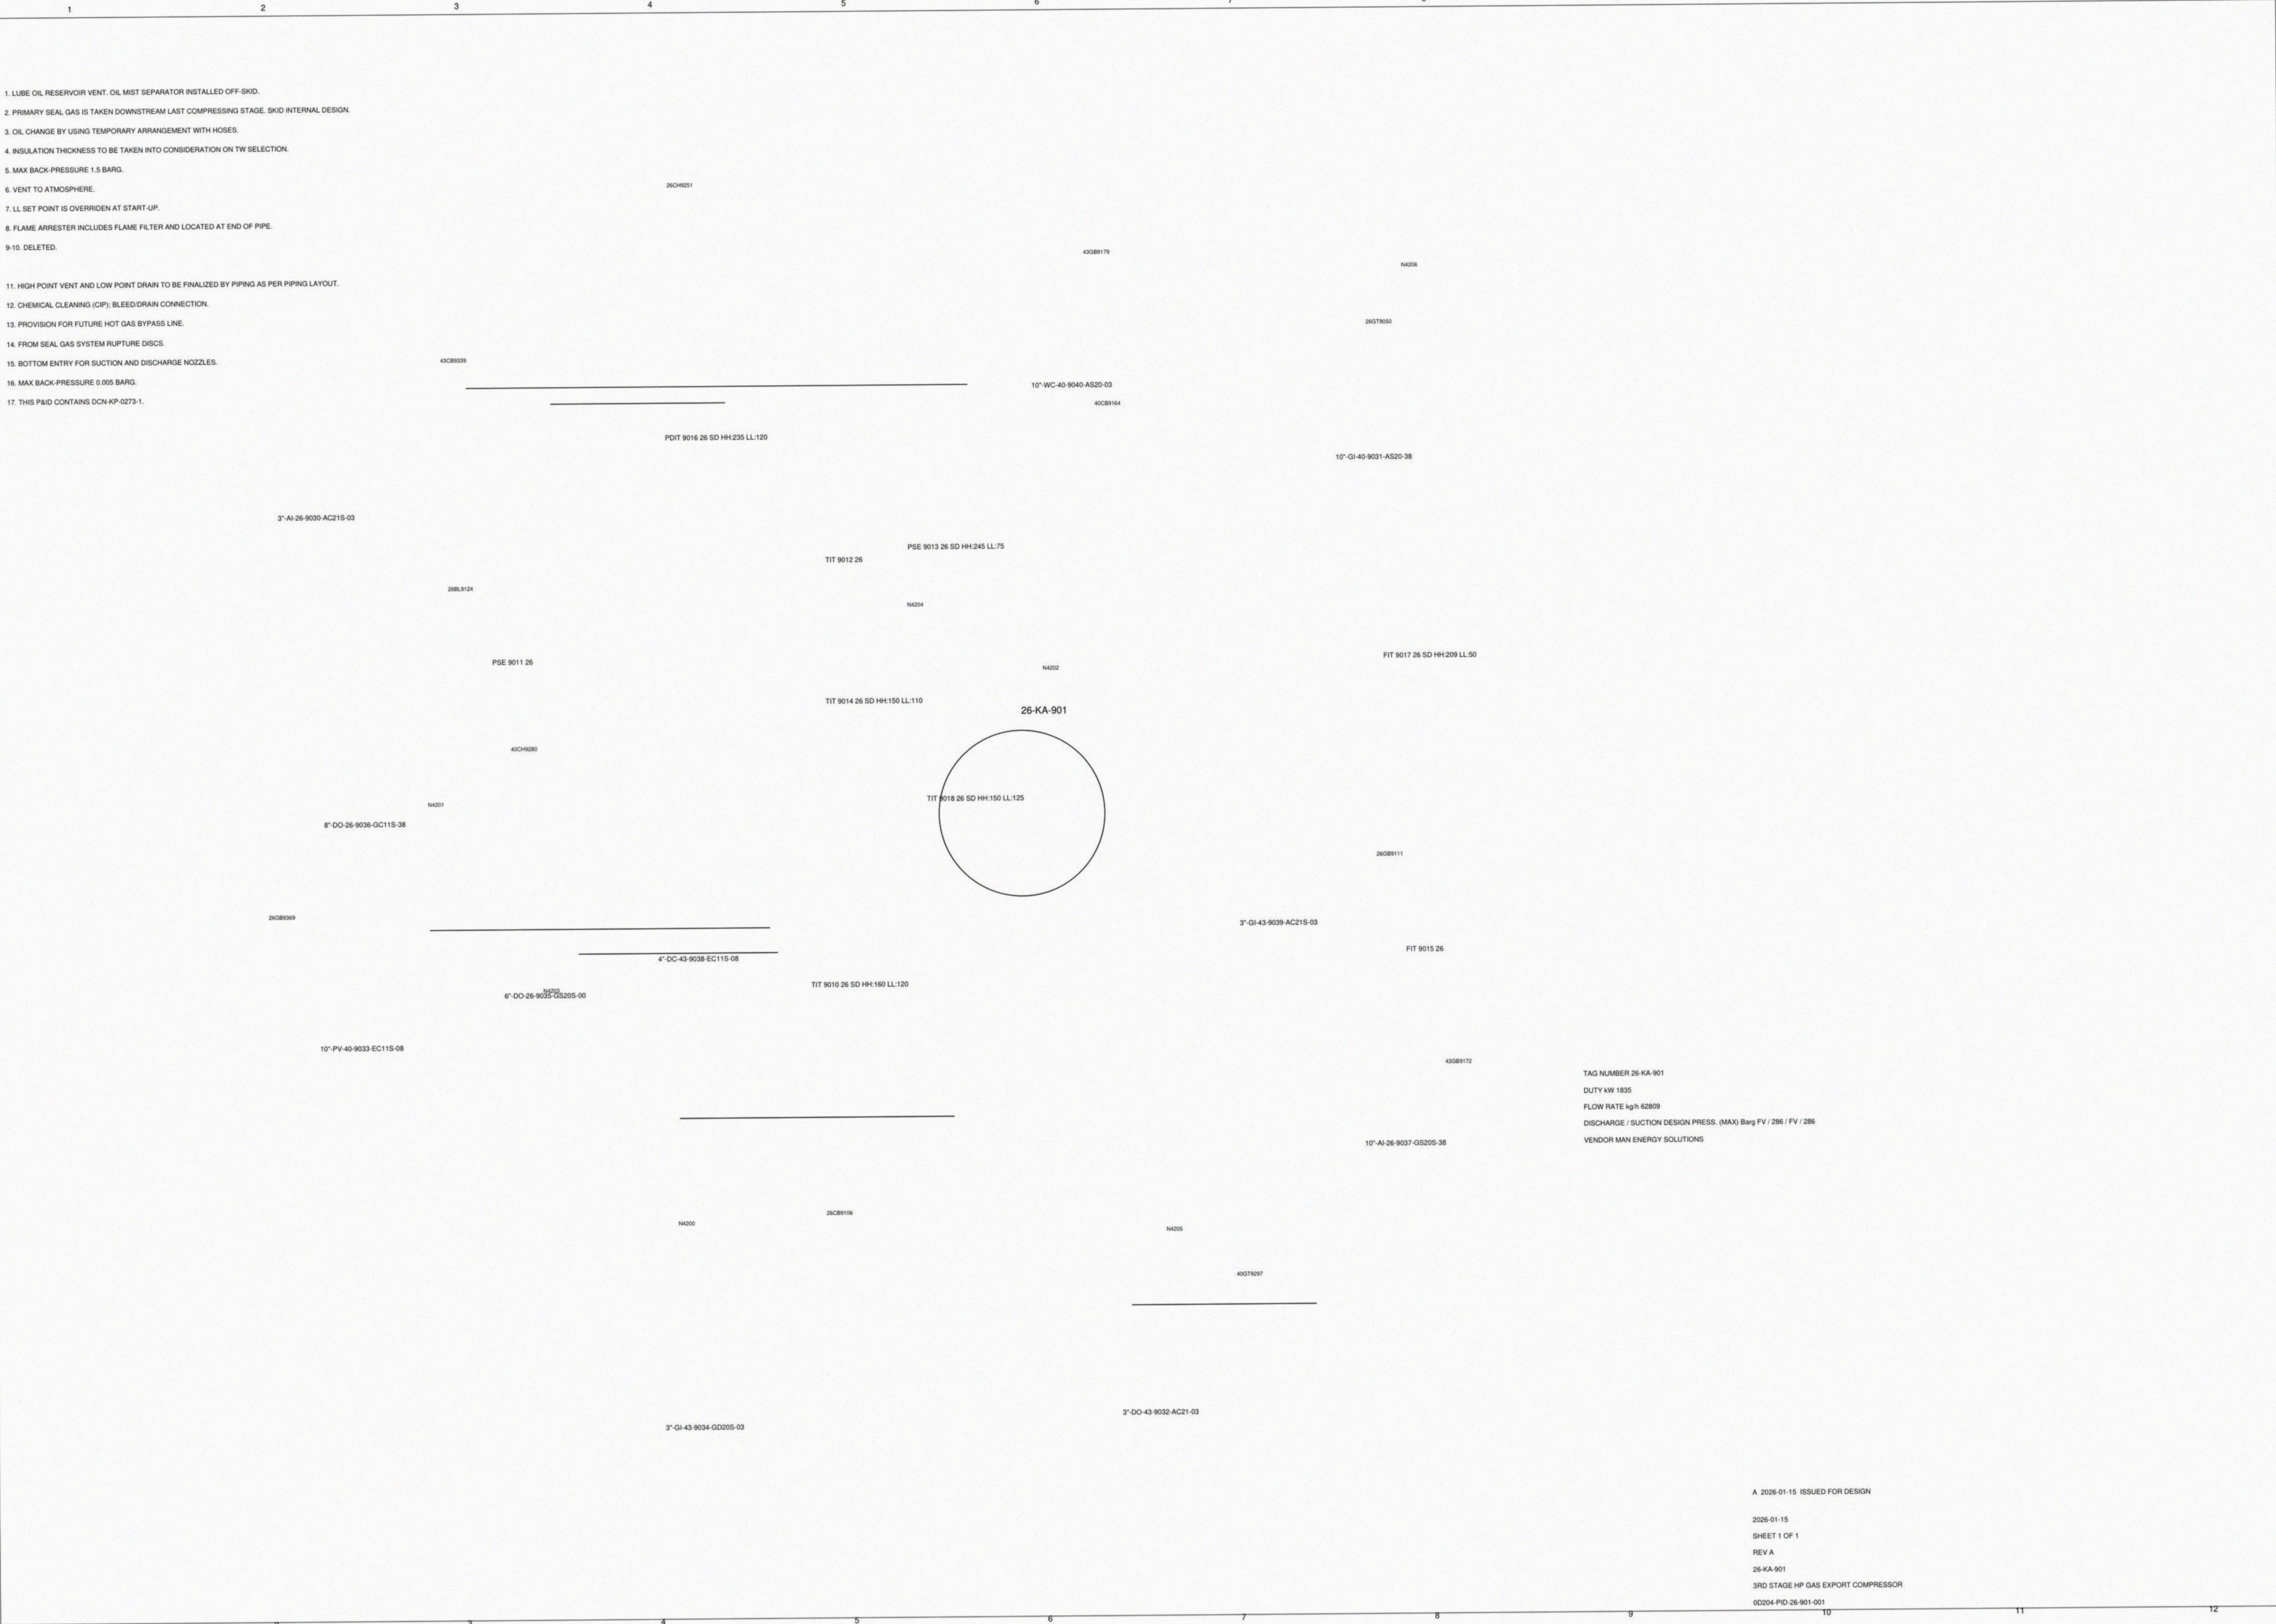

- 1. LUBE OIL RESERVOIR VENT. OIL MIST SEPARATOR INSTALLED OFF-SKID.
- 2. PRIMARY SEAL GAS IS TAKEN DOWNSTREAM LAST COMPRESSING STAGE. SKID INTERNAL DESIGN.
- 3. OIL CHANGE BY USING TEMPORARY ARRANGEMENT WITH HOSES.
- 4. INSULATION THICKNESS TO BE TAKEN INTO CONSIDERATION ON TW SELECTION.
- 5. MAX BACK-PRESSURE 1.5 BARG.
- 6. VENT TO ATMOSPHERE.
- 7. LL SET POINT IS OVERRIDEN AT START-UP.
- 8. FLAME ARRESTER INCLUDES FLAME FILTER AND LOCATED AT END OF PIPE.
- 9-10. DELETED.
- 11. HIGH POINT VENT AND LOW POINT DRAIN TO BE FINALIZED BY PIPING AS PER PIPING LAYOUT.
- 12. CHEMICAL CLEANING (CIP); BLEED/DRAIN CONNECTION.
- 13. PROVISION FOR FUTURE HOT GAS BYPASS LINE.
- 14. FROM SEAL GAS SYSTEM RUPTURE DISCS.
- 15. BOTTOM ENTRY FOR SUCTION AND DISCHARGE NOZZLES.
- 16. MAX BACK-PRESSURE 0.005 BARG.
- 17. THIS P&ID CONTAINS DCN-KP-0273-1.

TAG NUMBER 26-KA-901
DUTY kW 1835
FLOW RATE kg/h 62909
DISCHARGE / SUCTION DESIGN PRESS. (MAX) Barg FV / 286 / FV / 286
VENDOR MAN ENERGY SOLUTIONS